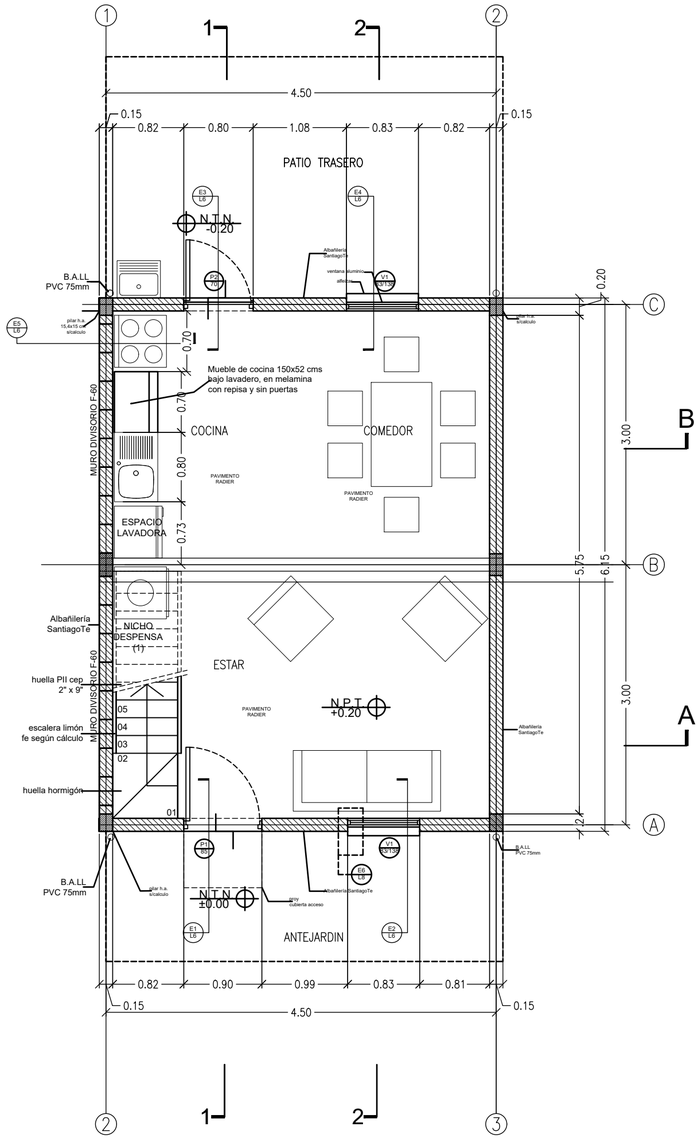
PATIO TRASERO
N.T.N.
-0.20
B.A.LL.
PVC 75mm
Mueble de cocina 150x52 cms
bajo lavadero, en melamina
con repisa y sin puertas
COCINA
COMEDOR
MURO DIVISORIO F-60
ESPACIO
LAVADORA
Albañilería
SantiagoTe
NICHO
DESPENSA
(1)
ESTAR
N.P.T.
+0.20
huella PII cep
2" x 9"
escalera limón
fe según cálculo
huella hormigón
N.T.N.
±0.00
ANTEJARDIN
4.50
0.15
0.82
0.80
1.08
0.83
0.82
0.90
0.99
0.81
3.00
6.15
5.75
2.4

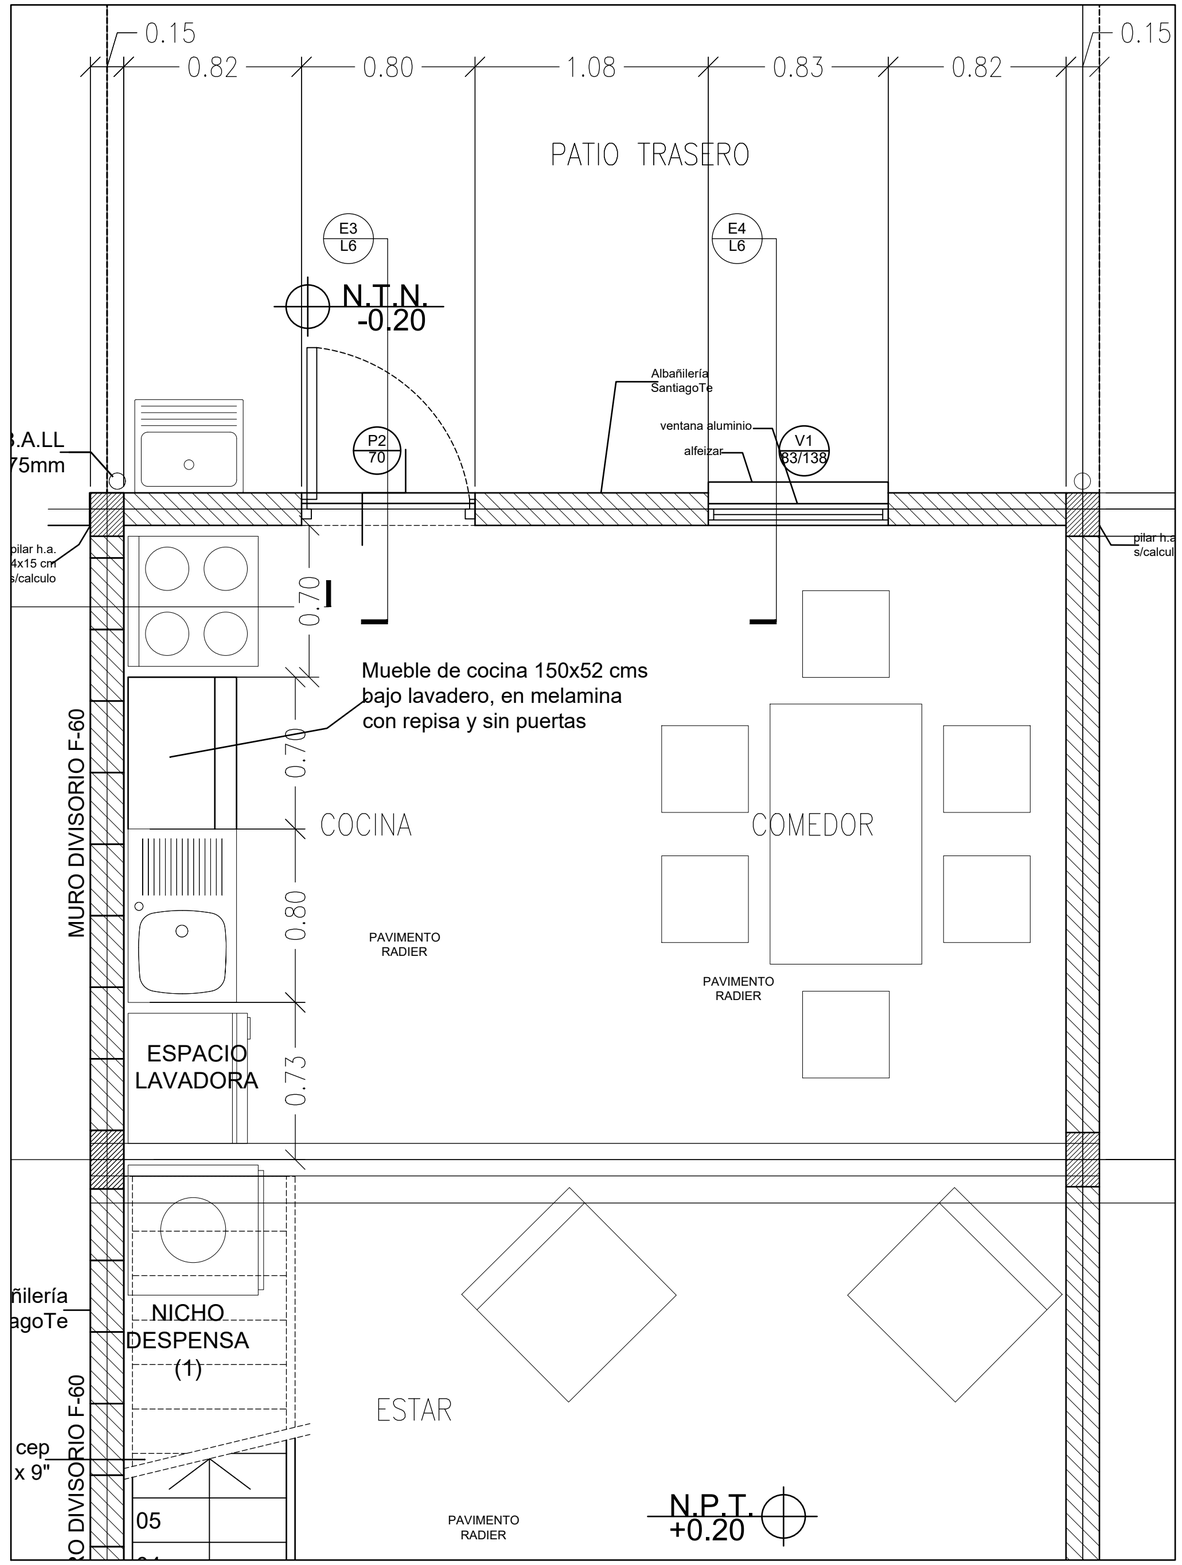
0.15
0.82
0.80
1.08
0.83
0.82
PATIO TRASERO
E3
L6
E4
L6
N.T.N.
-0.20
Albañilería
SantiagoTe
ventana aluminio
alfeizar
V1
83/138
P2
70
B.A.LL
75mm
pilar h.a.
4x15 cm
s/calculo
Mueble de cocina 150x52 cms
bajo lavadero, en melamina
con repisa y sin puertas
MURO DIVISORIO F-60
COCINA
COMEDOR
PAVIMENTO
RADIER
ESPACIO
LAVADORA
NICHO
DESPENSA
(1)
ESTAR
N.P.T.
+0.20
0.70
0.80
0.73