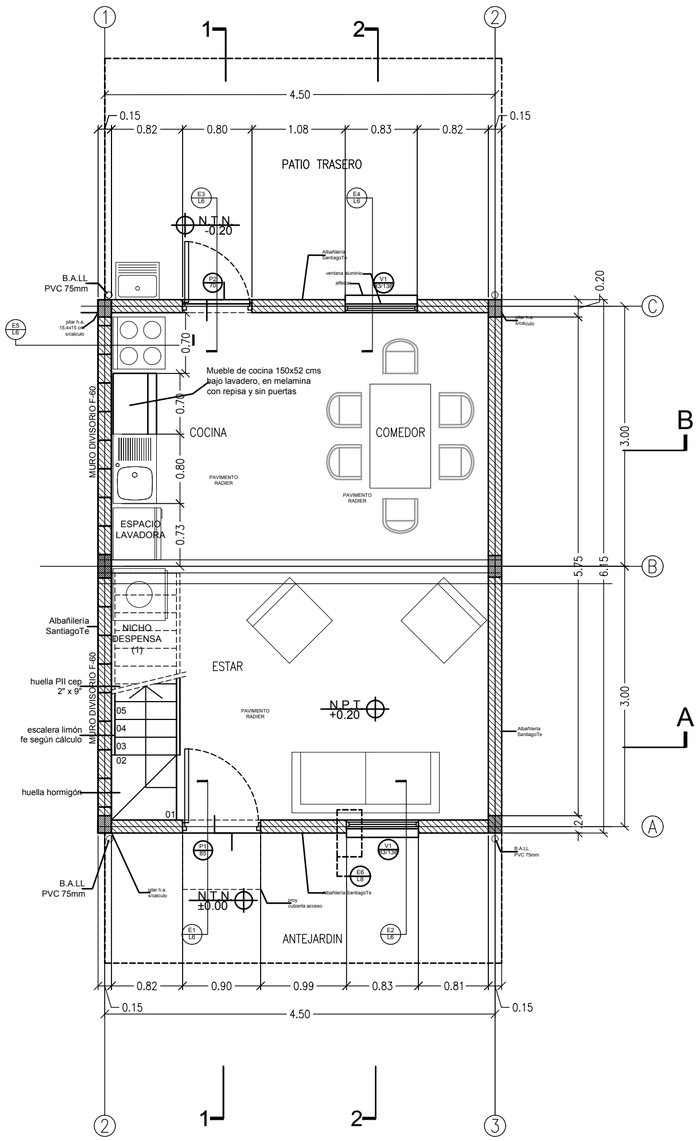
PATIO TRASERO
N.T.N.
-0.20
B.A.LL.
PVC 75mm
Mueble de cocina 150x52 cms
bajo lavadero, en melamina
con repisa y sin puertas
COCINA
COMEDOR
MURO DIVISORIO F-60
ESPACIO
LAVADORA
NICHO
DESPENSA
(1)
ESTAR
N.P.T.
+0.20
huella PII ceg
2" x 9"
escalera limón
fe según cálculo
huella hormigón
N.T.N.
±0.00
ANTEJARDIN
Albañilería
SantiagoTe
4.50
0.15
0.82
0.80
1.08
0.83
0.82
0.90
0.99
0.81
3.00
5.75
6.15
0.20
0.70
0.80
0.73

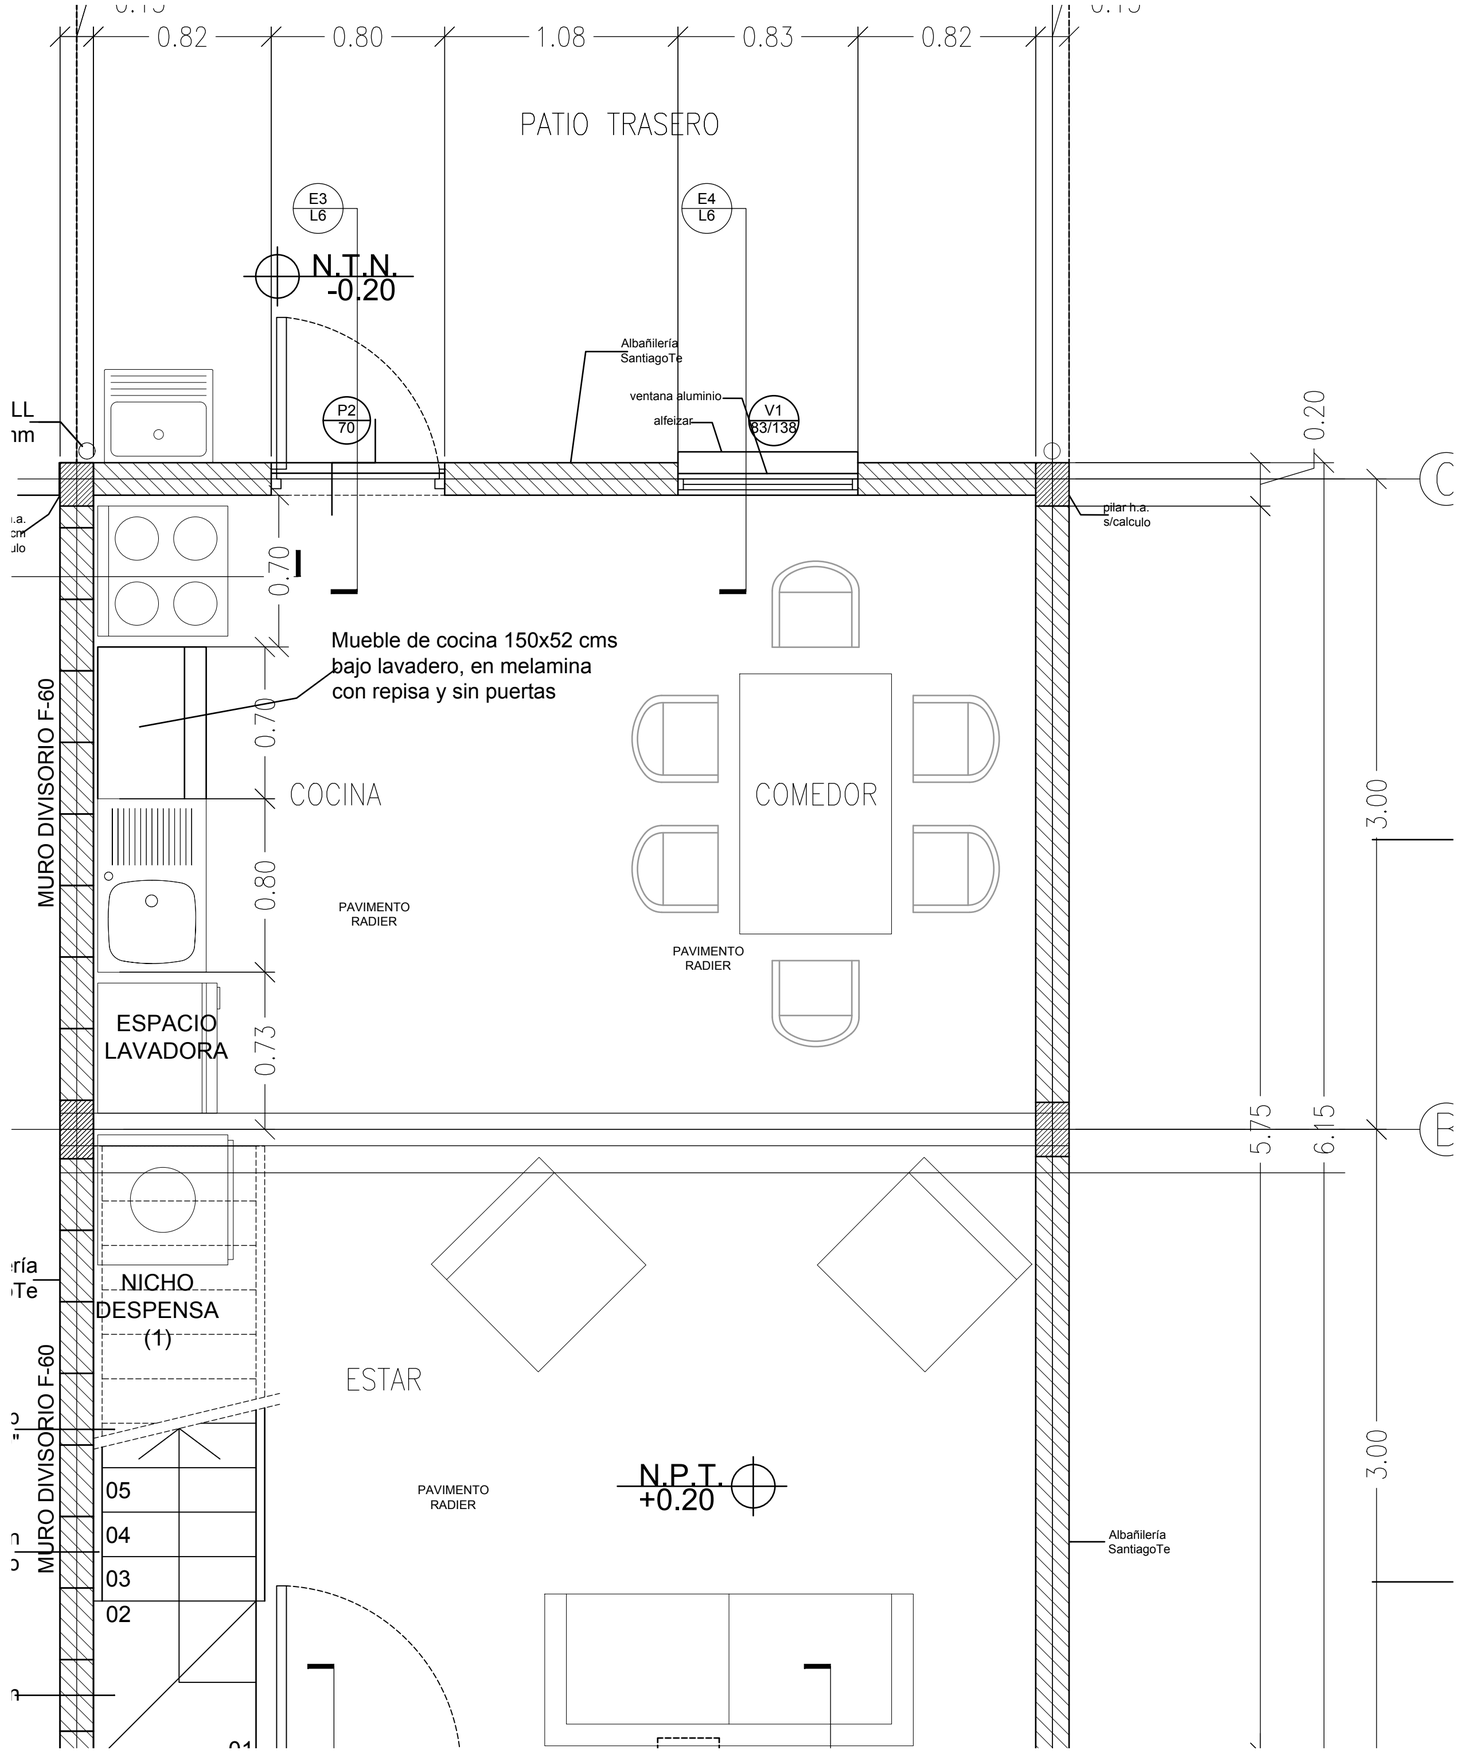
PATIO TRASERO
E3
L6
E4
L6
N.T.N.
-0.20
P2
70
V1
33/138
Albañilería
SantiagoTe
ventana aluminio
alfeizar
pilar h.a.
s/calculo
Mueble de cocina 150x52 cms
bajo lavadero, en melamina
con repisa y sin puertas
COCINA
COMEDOR
MURO DIVISORIO F-60
ESPACIO
LAVADORA
NICHO
DESPENSA
(1)
ESTAR
PAVIMENTO
RADIER
N.P.T.
+0.20
05
04
03
02
0.82
0.80
1.08
0.83
0.82
0.70
0.80
0.73
0.20
3.00
5.75
6.15